


1 этаж

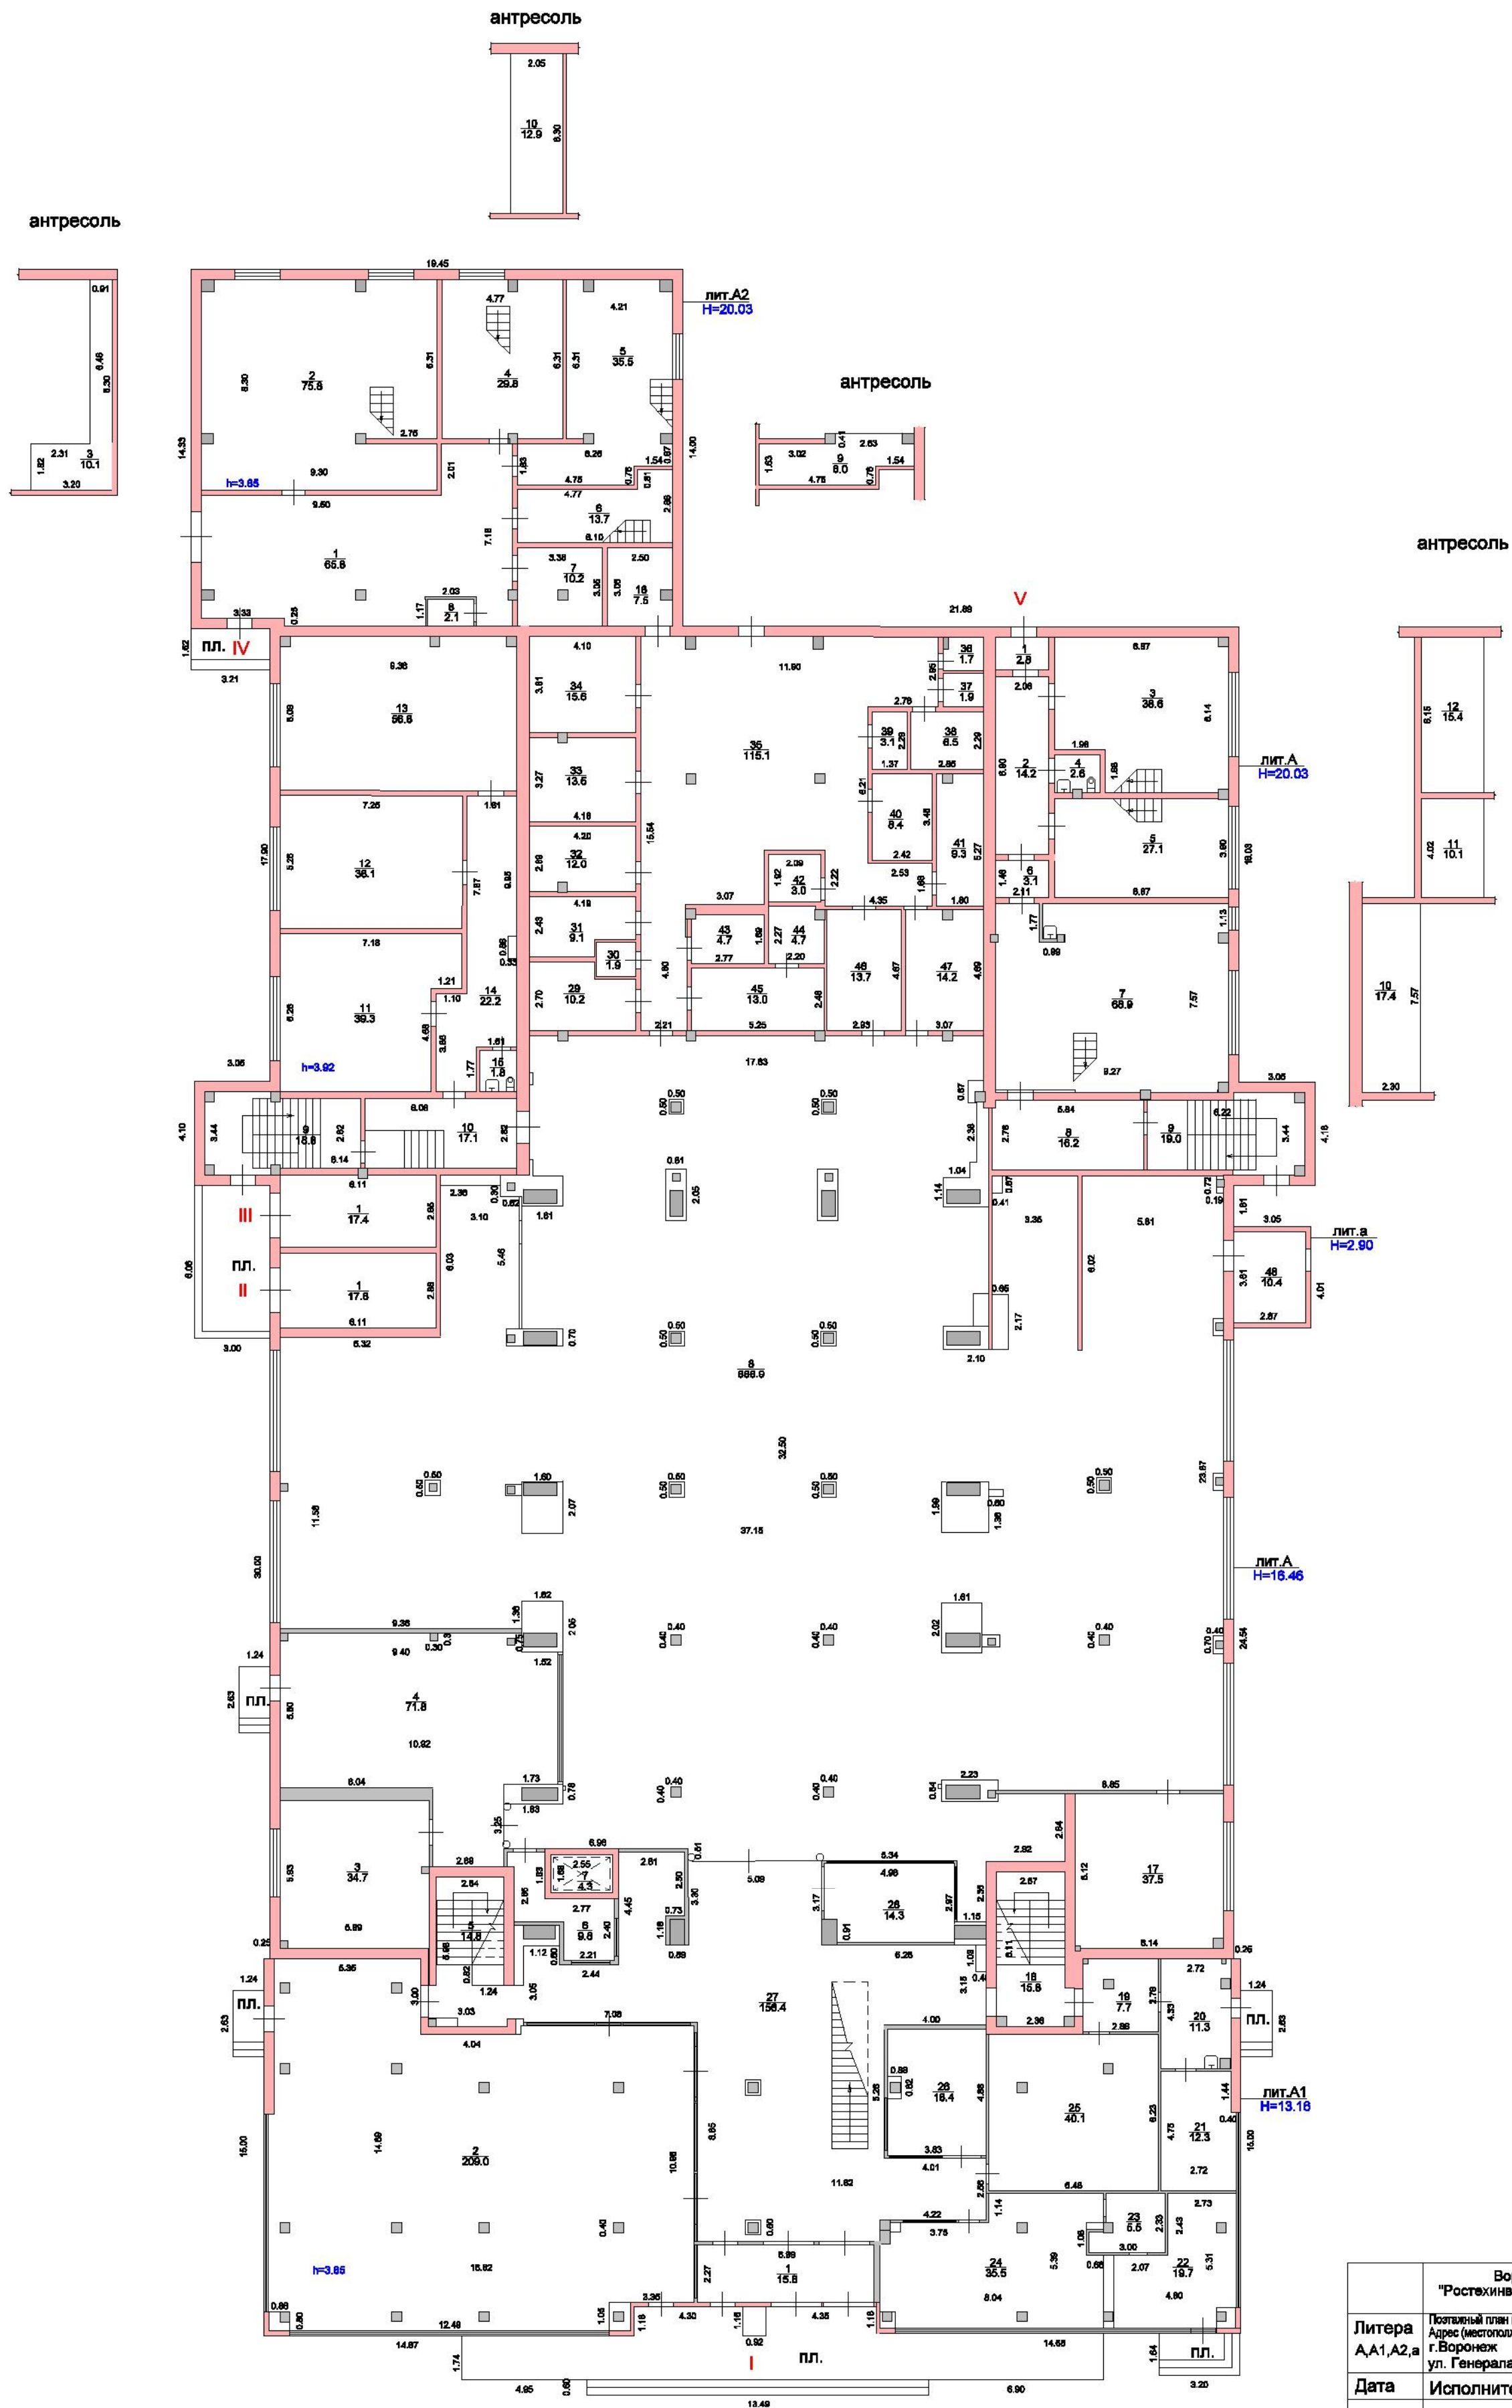

	Воронежский филиал ГФУП "Ростехинвентаризация-Федеральное БТИ"		Инва. № 10342
Литера А.А1,А2,а	Постыльный план на здание (строение) Адрес (использование) г. Воронеж ул. Генерала Лизюкова, 50		М 1:200
Дата	Исполнитель	Фамилия, имя, отчество	Подпись
22.04.2013	Исполнил	Бабенкова Т.А.	
	Проверил	Горелкая Т.В.	
22.04.2013	Директор	Зарубин А.В.	